


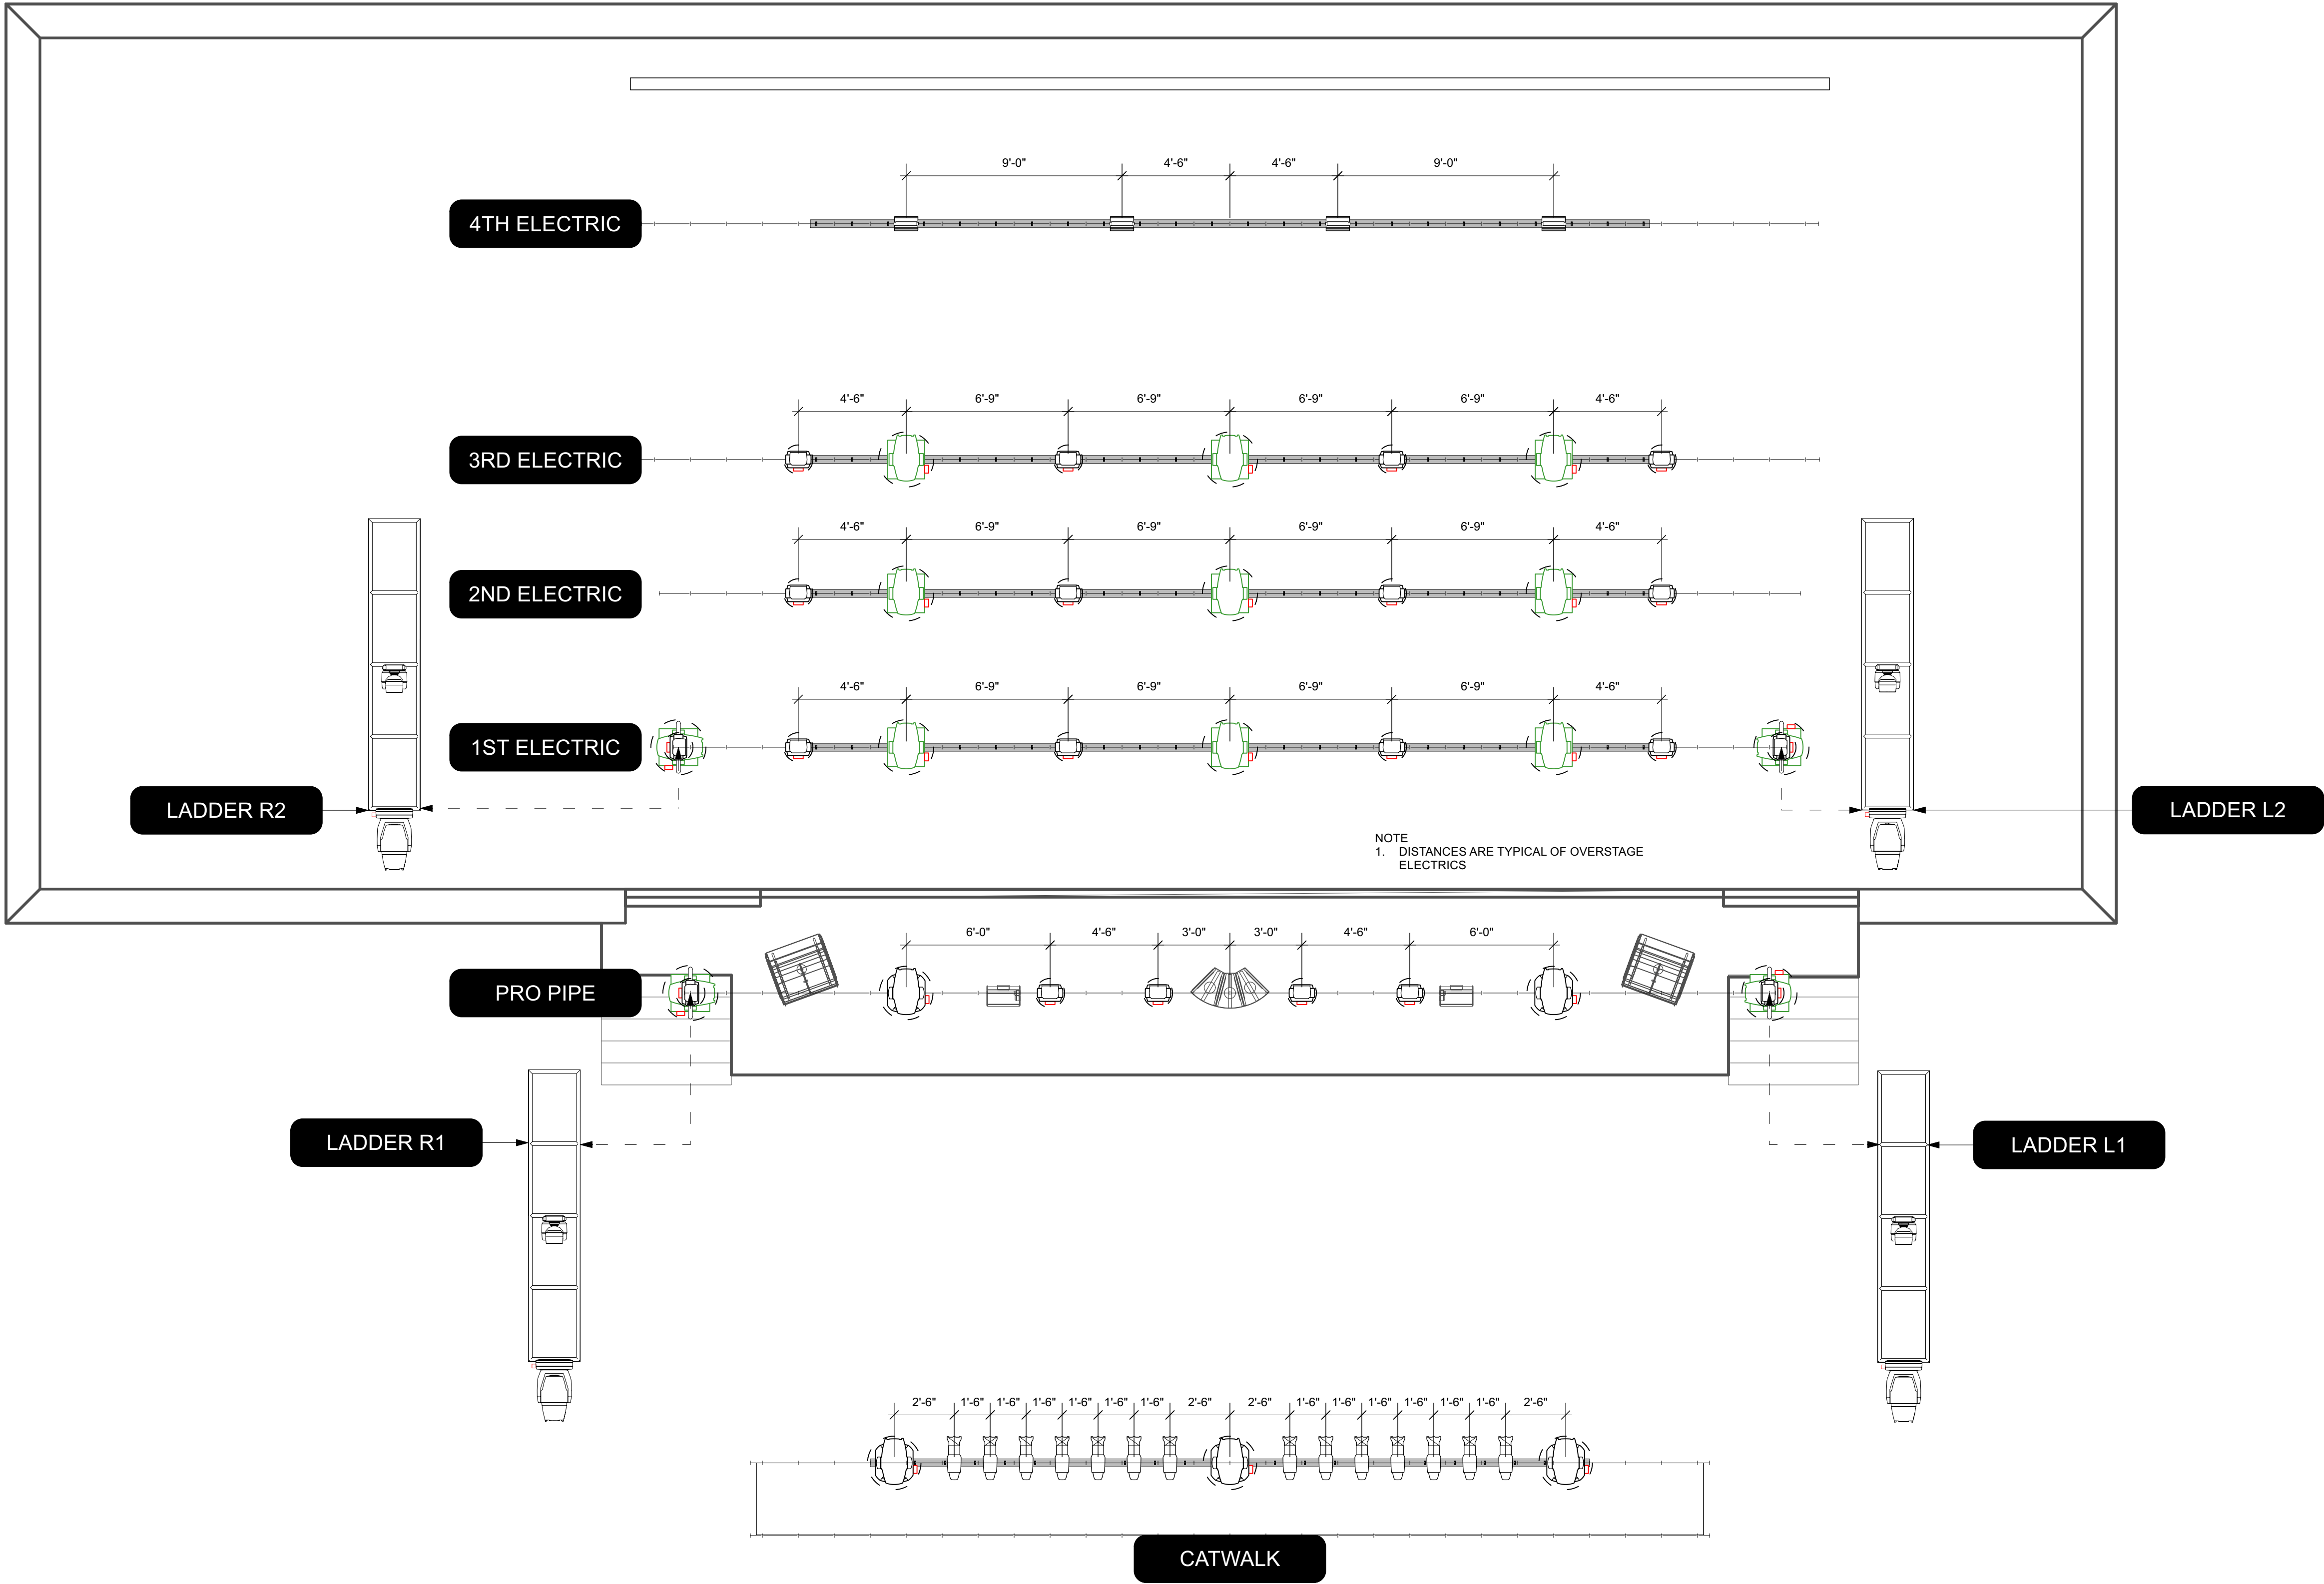

Symbol Key		
INTELLIGENT LIGHTS		
	SGM G-PROFILE	5
	SGM G-SPOT	13
	19X15W RGBW WASH ZOOM	20
	ALTMAN SPECTRA CYC 100	8
CONVENTIONALS		
	ETC S4 19DEG	8
	ETC S4 26DEG	6
TYPICAL		

TITLE		
PLAN VIEW		
PLATE	DRAWN BY	DATE
1 / 14	ADAM MANNING	1/25/21
PROJECT NAME		
THS HAFEN REP 2021		