


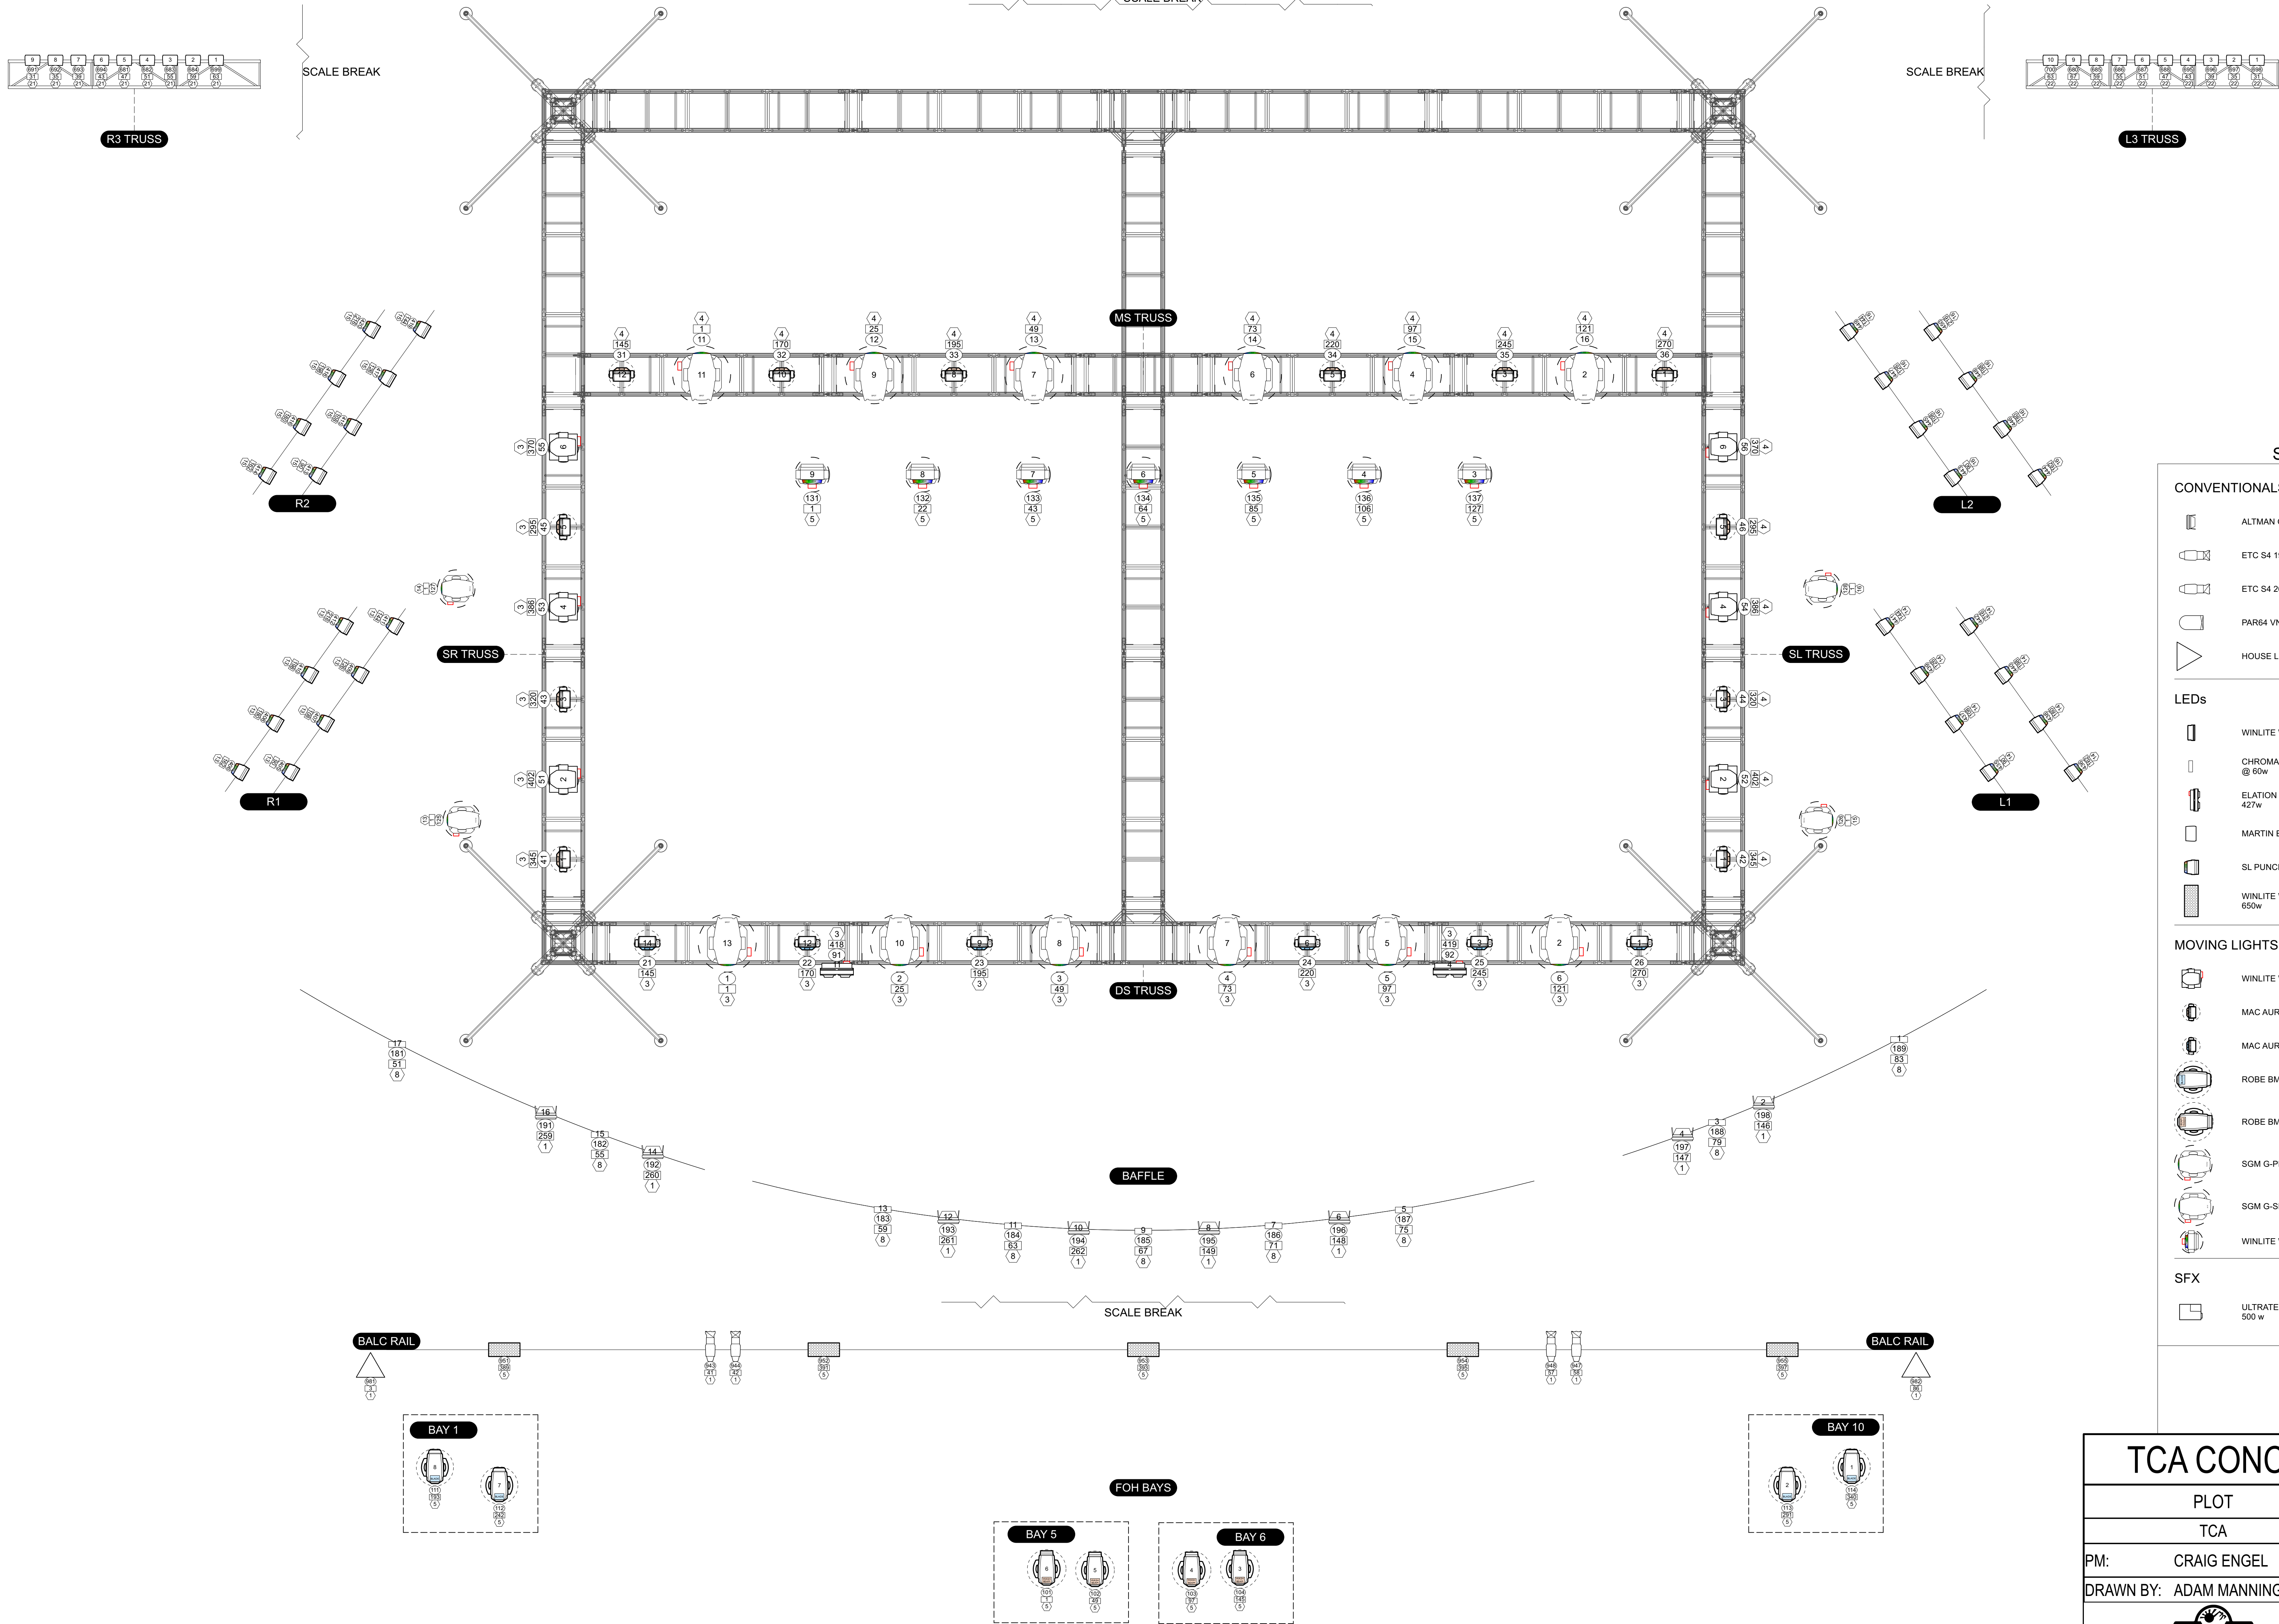

Symbol Key		
CONVENTIONALS		
	ALTMAN Q LITE @ 1kw	14
	ETC S4 190DEG @ 575w	2
	ETC S4 260DEG @ 575w	6
	PAR64 VNSP @ 1KW	72
	HOUSE LIGHT	2
LEDs		
	WINLITE WPO-14 @ 150w	7
	CHROMAQ COLORFORCE COMPACT @ 60w	9
	ELATION CUEPIX BLINDER WW4 @ 427w	2
	MARTIN EXT WASH 300 @ 300w	19
	SL PUNCHLITE 220 RGBW @ 220w	32
	WINLITE WCW 60x10 LED WASH @ 650w	12
MOVING LIGHTS		
	WINLITE WMB-230 @ 300w	6
	MAC AURA @ 260w	12
	MAC AURA XB @ 400w	6
	ROBE BMFL BLADE @ 1.7kw	4
	ROBE BMFL WASHBEAM @ 1.7kw	4
	SGM G-PROFILE @ 1.1kw	4
	SGM G-SPOT @ 1.1kw	12
	WINLITE WMZB-19 @ 330w	7
SFX		
	ULTRATECFX RADIANCE HAZER @ 500 w	4

TCA CONCERT PLOT

PLOT

TCA

PM: CRAIG ENGEL

DRAWN BY: ADAM MANNING

Date : 2/25/21

1 OF 12